



DEBUG OVERLAY LEGEND


- CH
- EM
- EMEM
- NORMAL
- marker_only

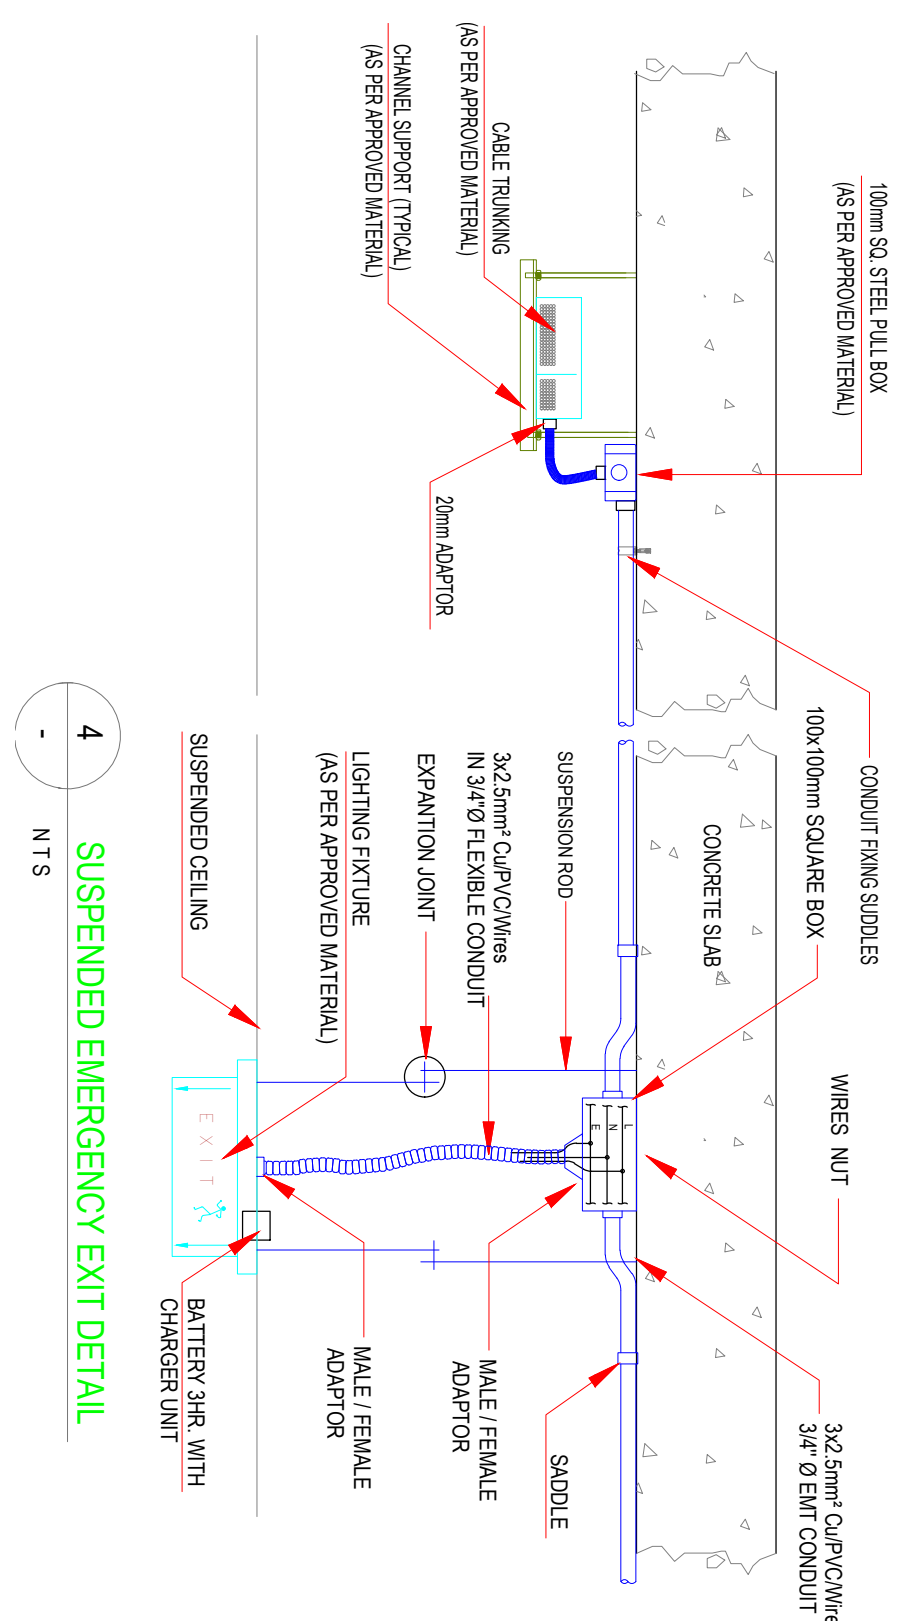

TYPICAL LIGHTING HOMERUN SECTION DETAILS

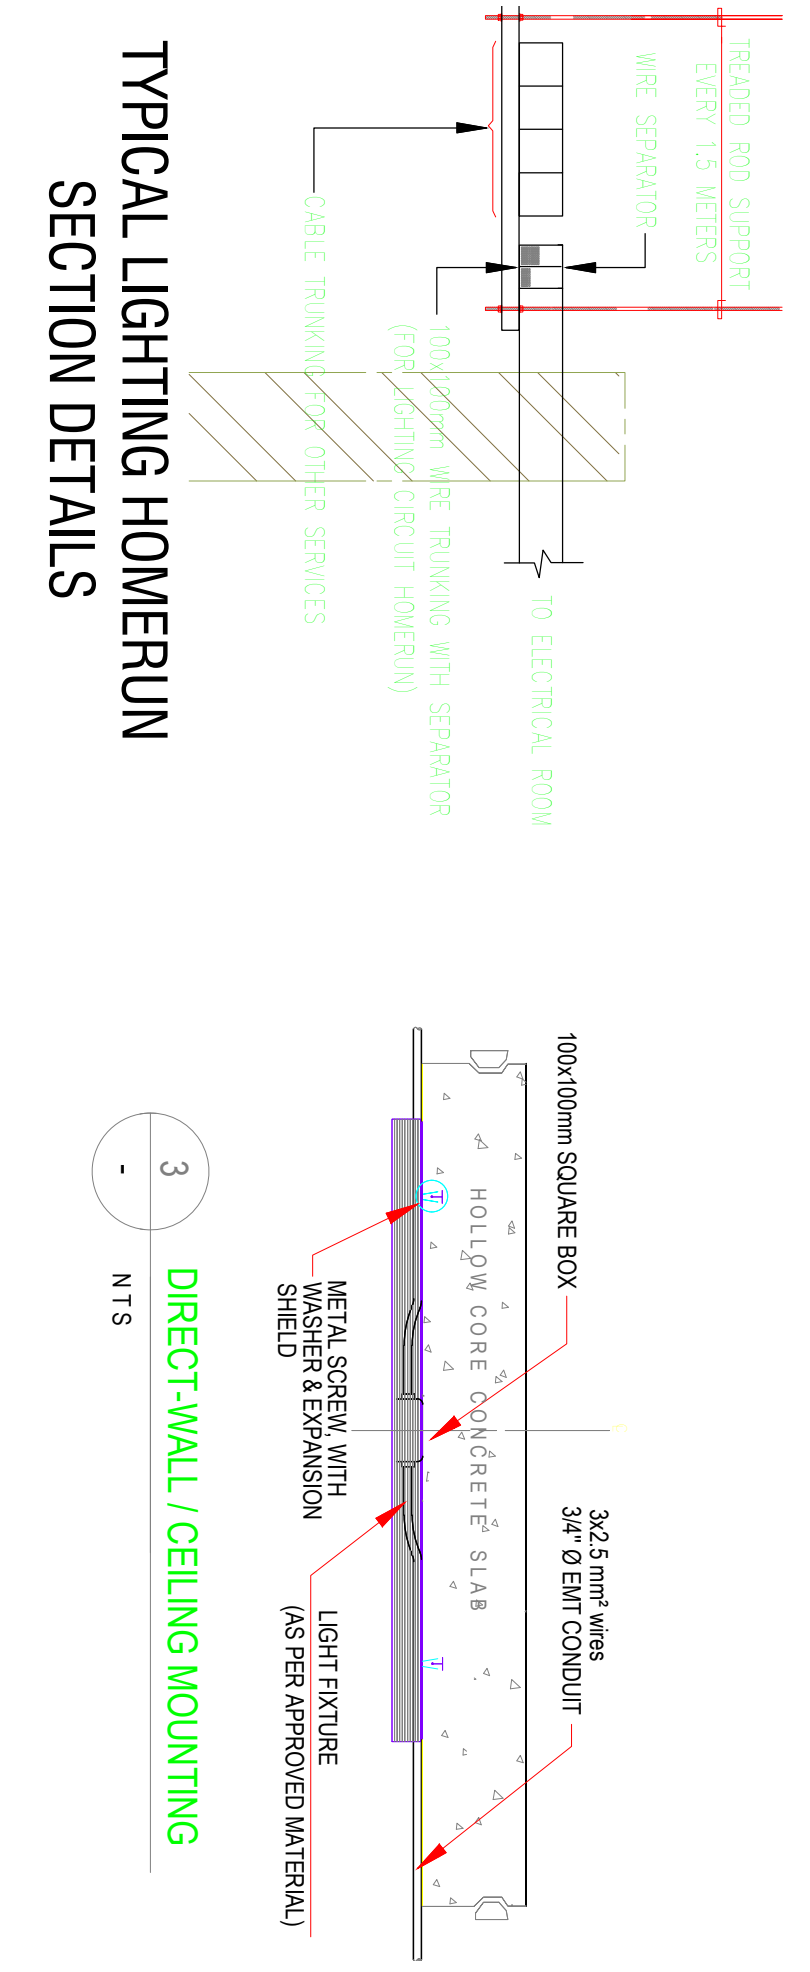

LIGHT SWITCH MOUNTING TYPICAL DETAIL

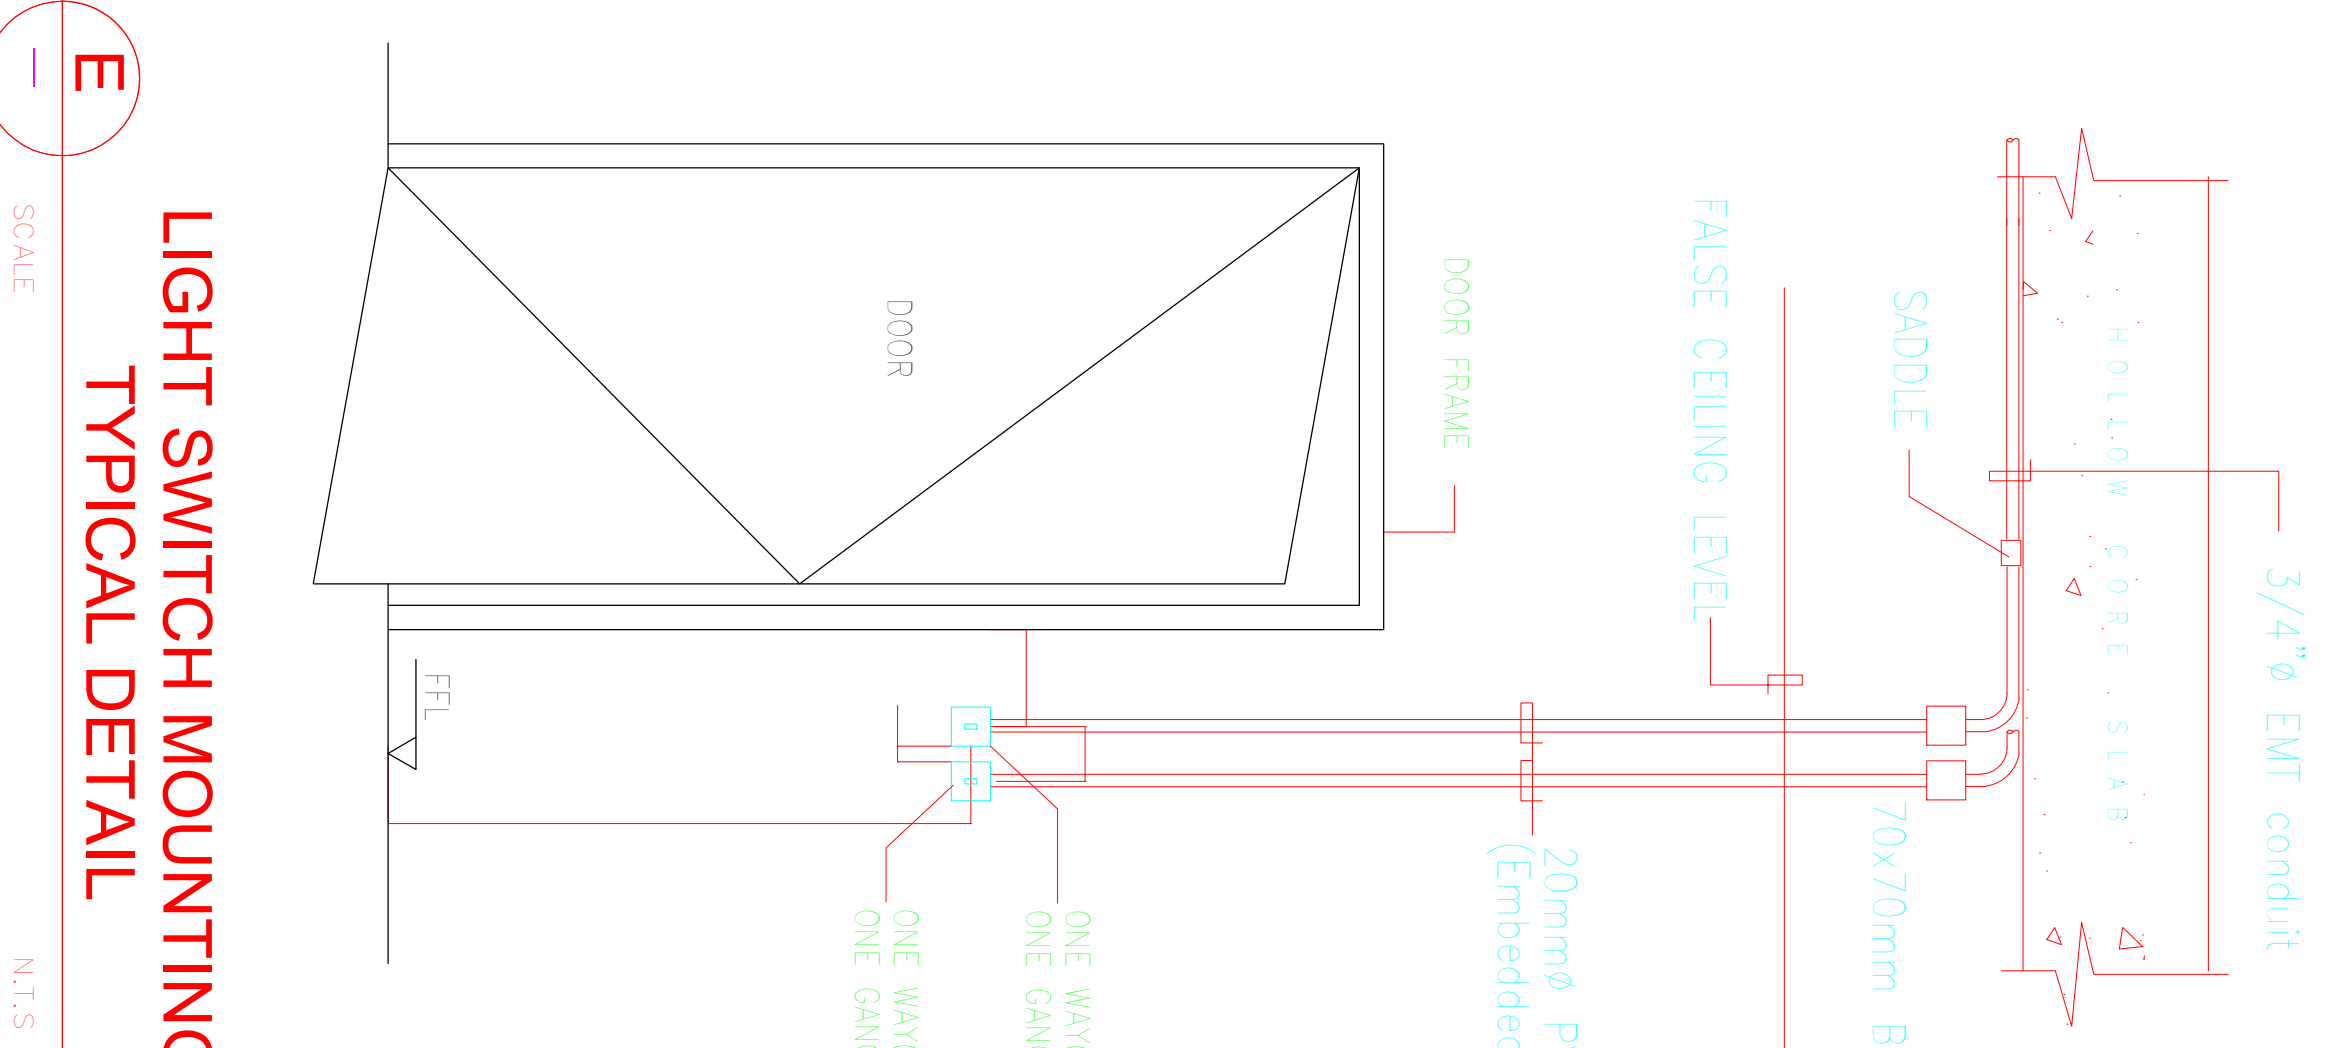

SCALE 1:15