




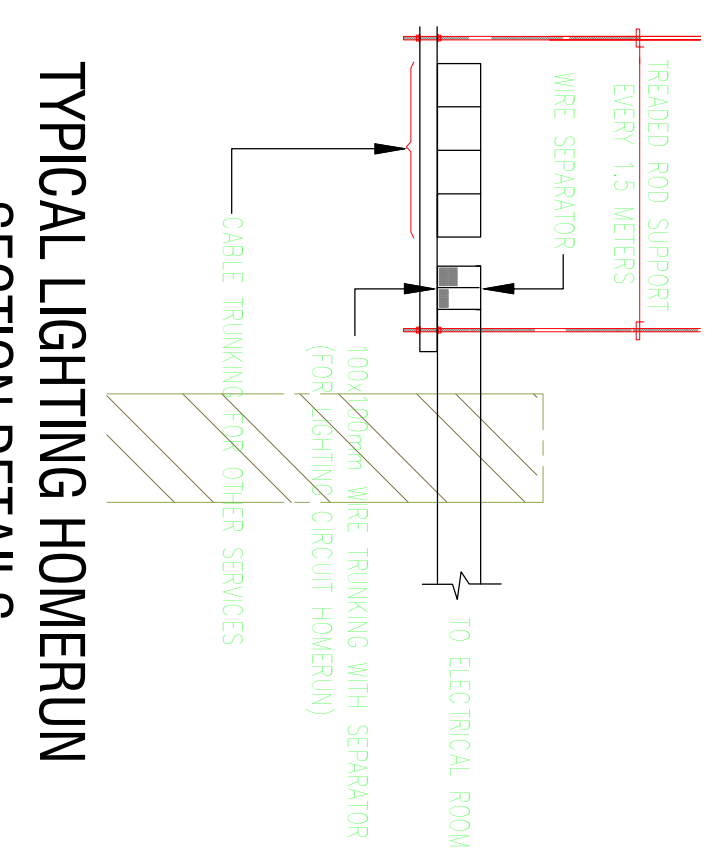


TYPICAL LIGHTING HOMERUN
SECTION DETAILS

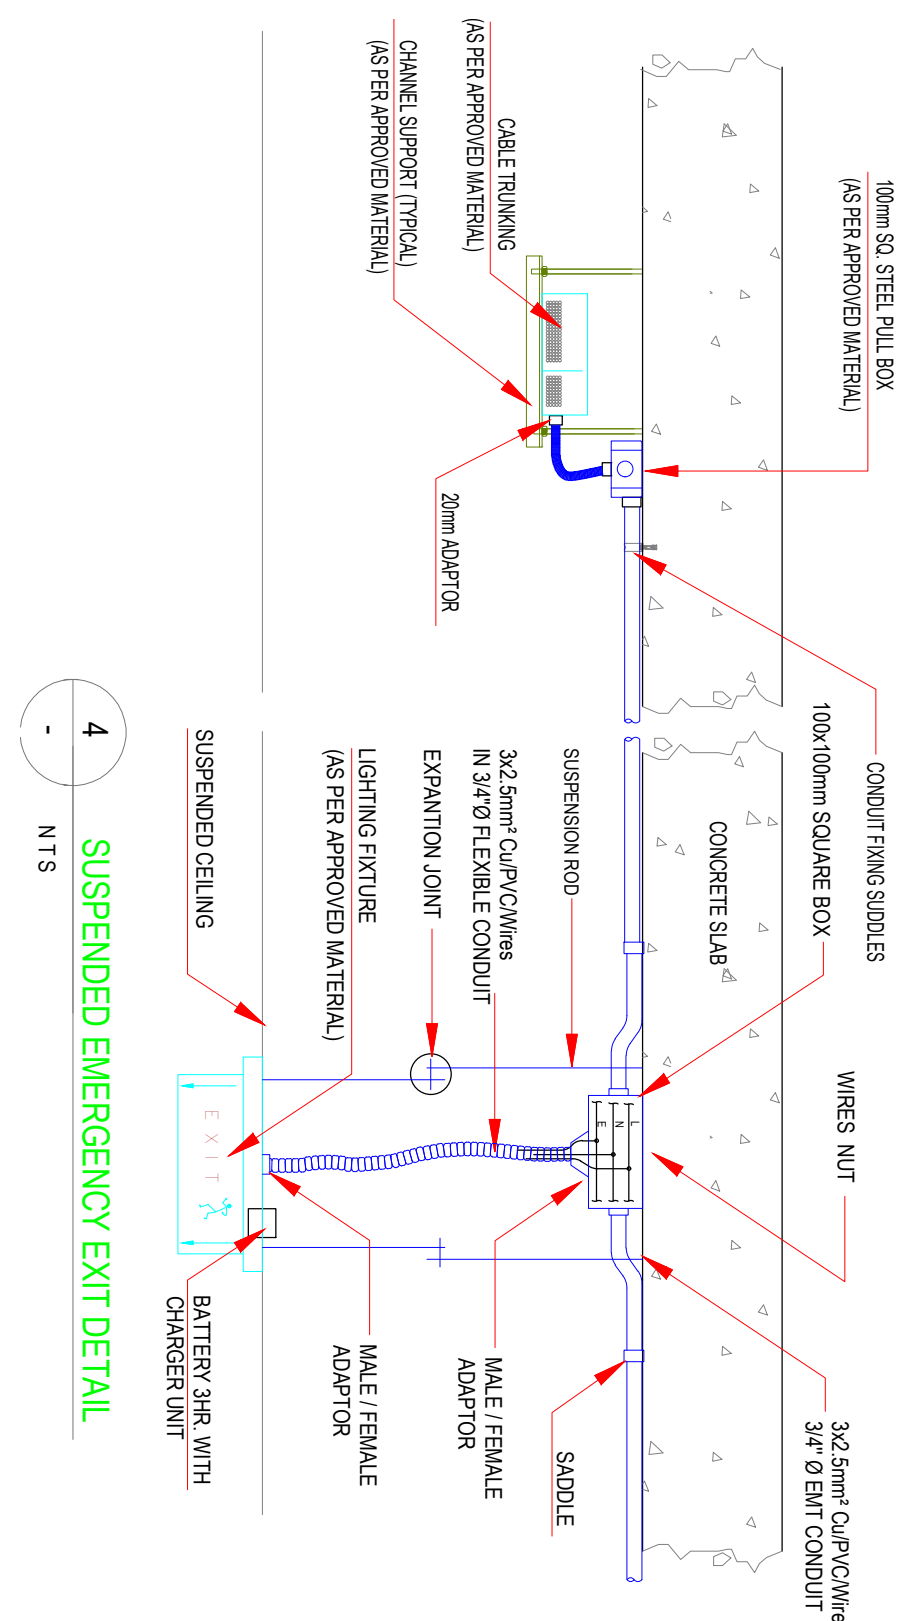


3
N.T.S.
DIRECT-WALL / CEILING MOUNTING

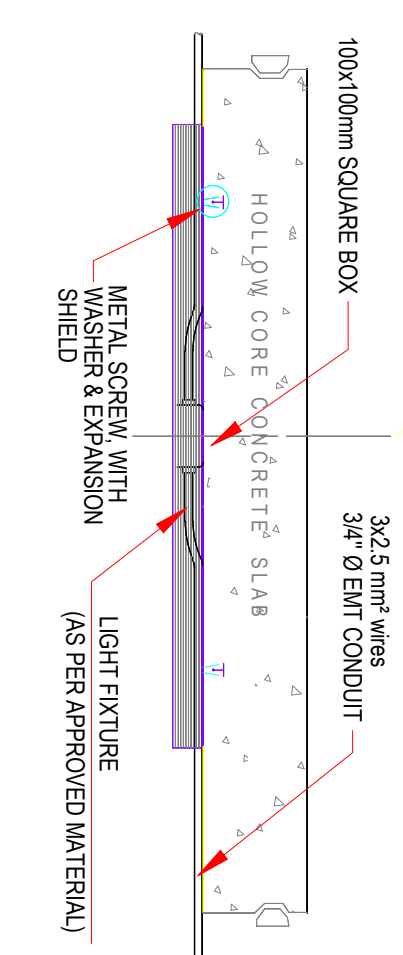

4
N.T.S.
SUSPENDED EMERGENCY EXIT DETAIL

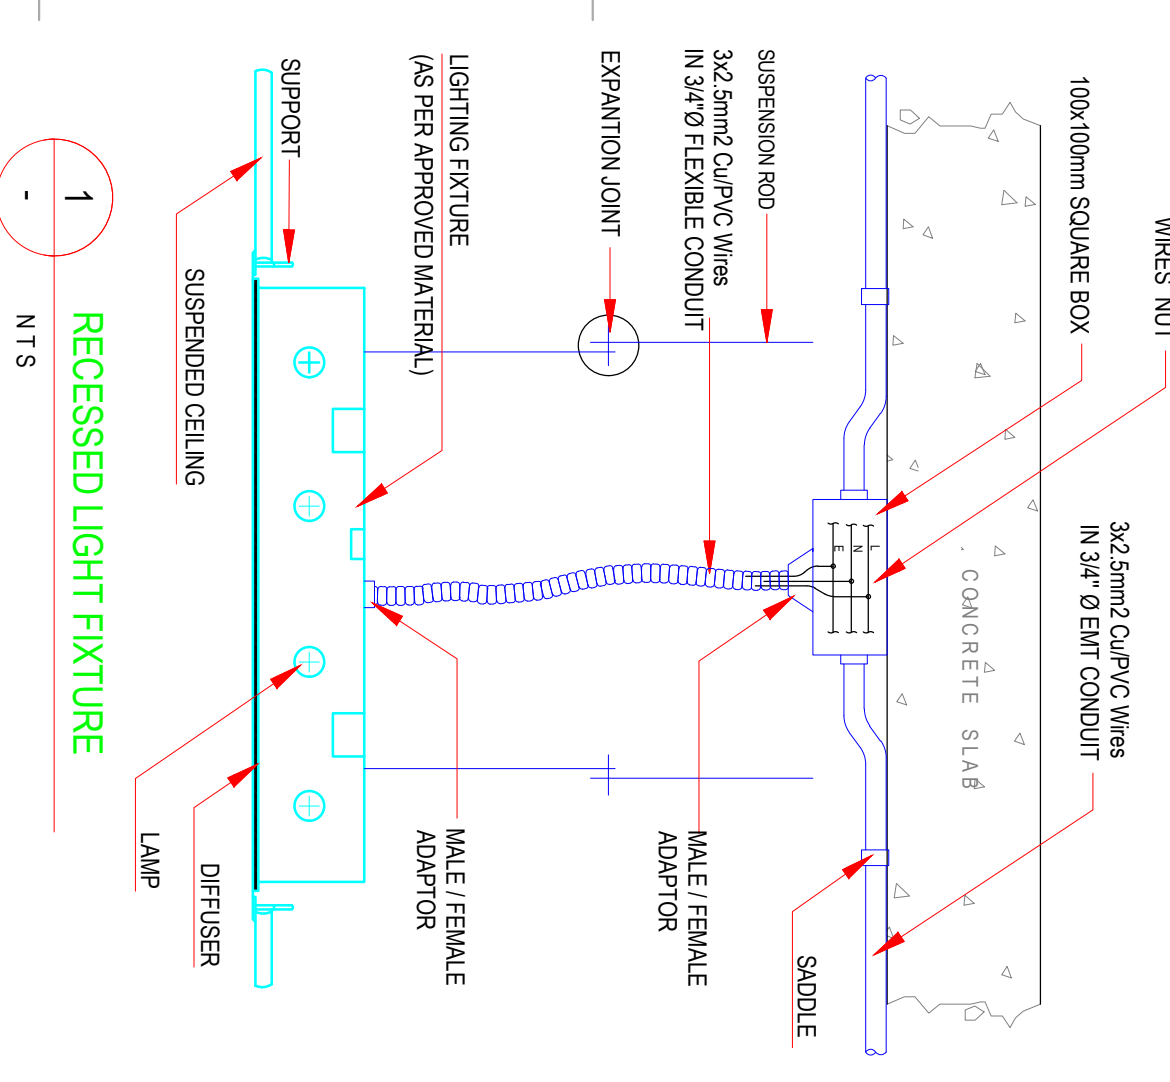

1
N.T.S.
RECESSED LIGHT FIXTURE

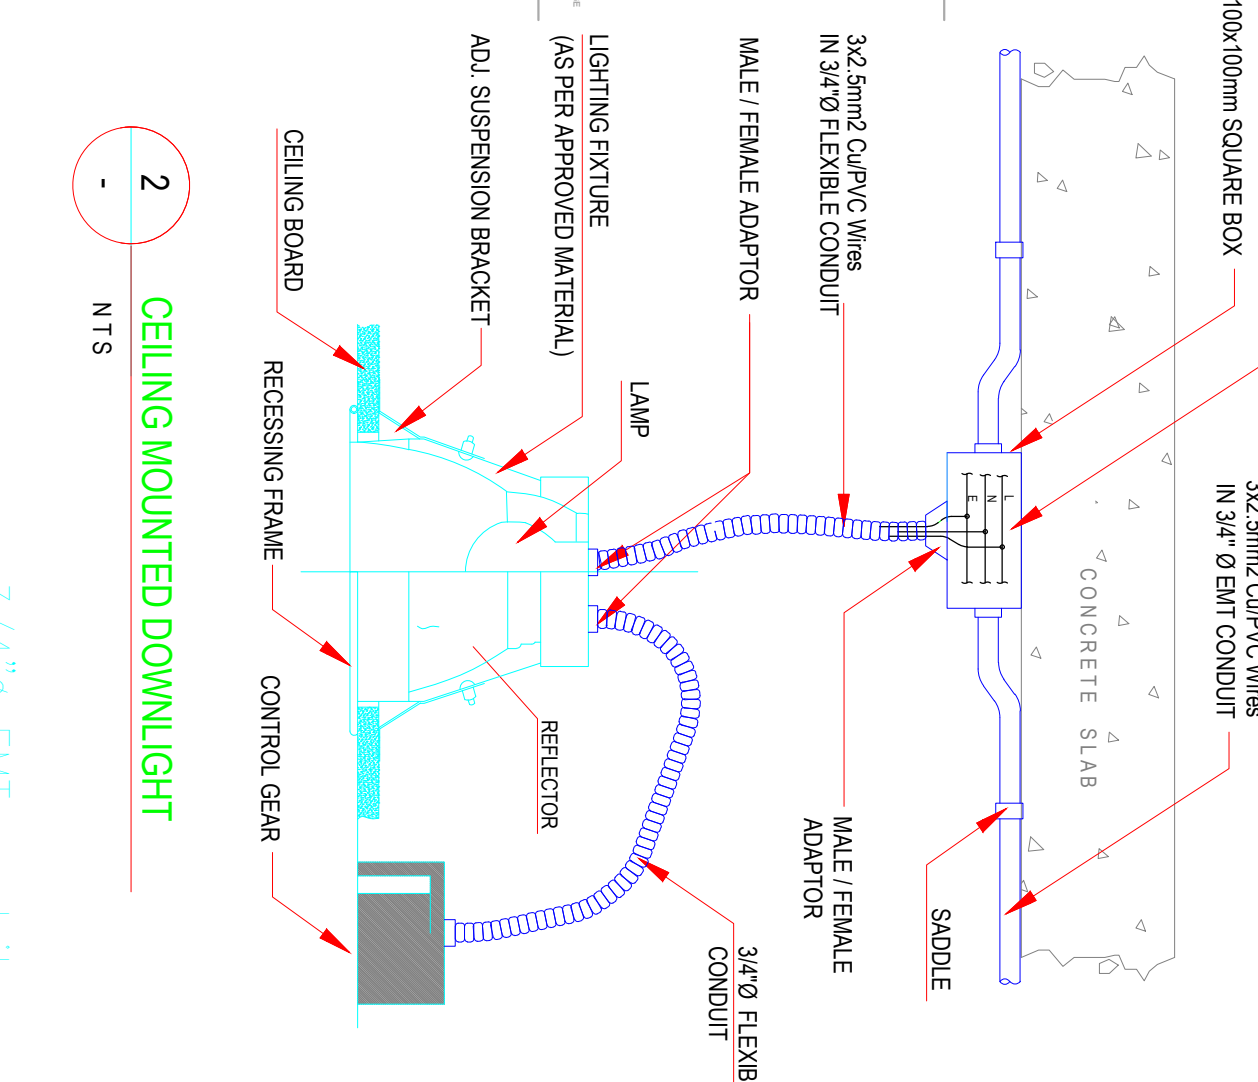

2
N.T.S.
CEILING MOUNTED DOWNLIGHT

E
SCALE
LIGHT SWITCH MOUNTING
TYPICAL DETAIL

20mm P/C (Embedded)
70x70mm Box
3/4\"/>