




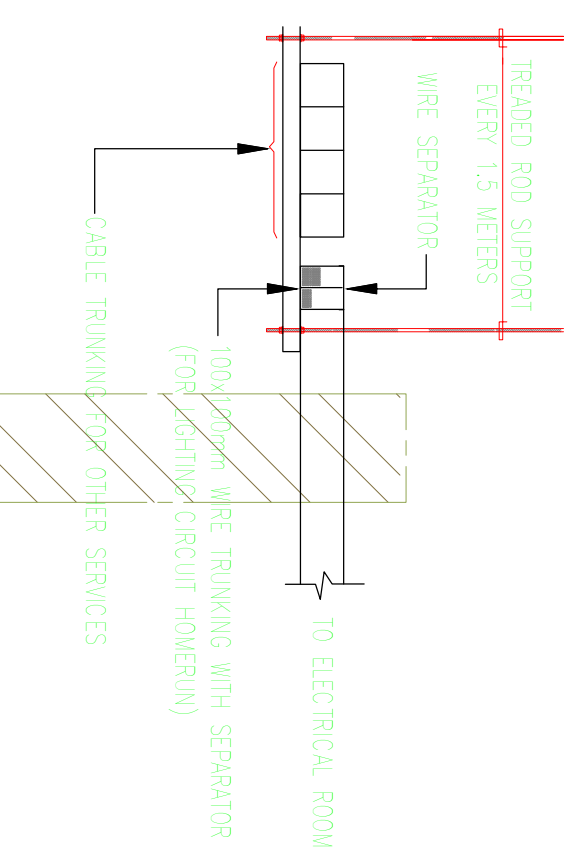


TYPICAL LIGHTING HOMERUN SECTION DETAILS

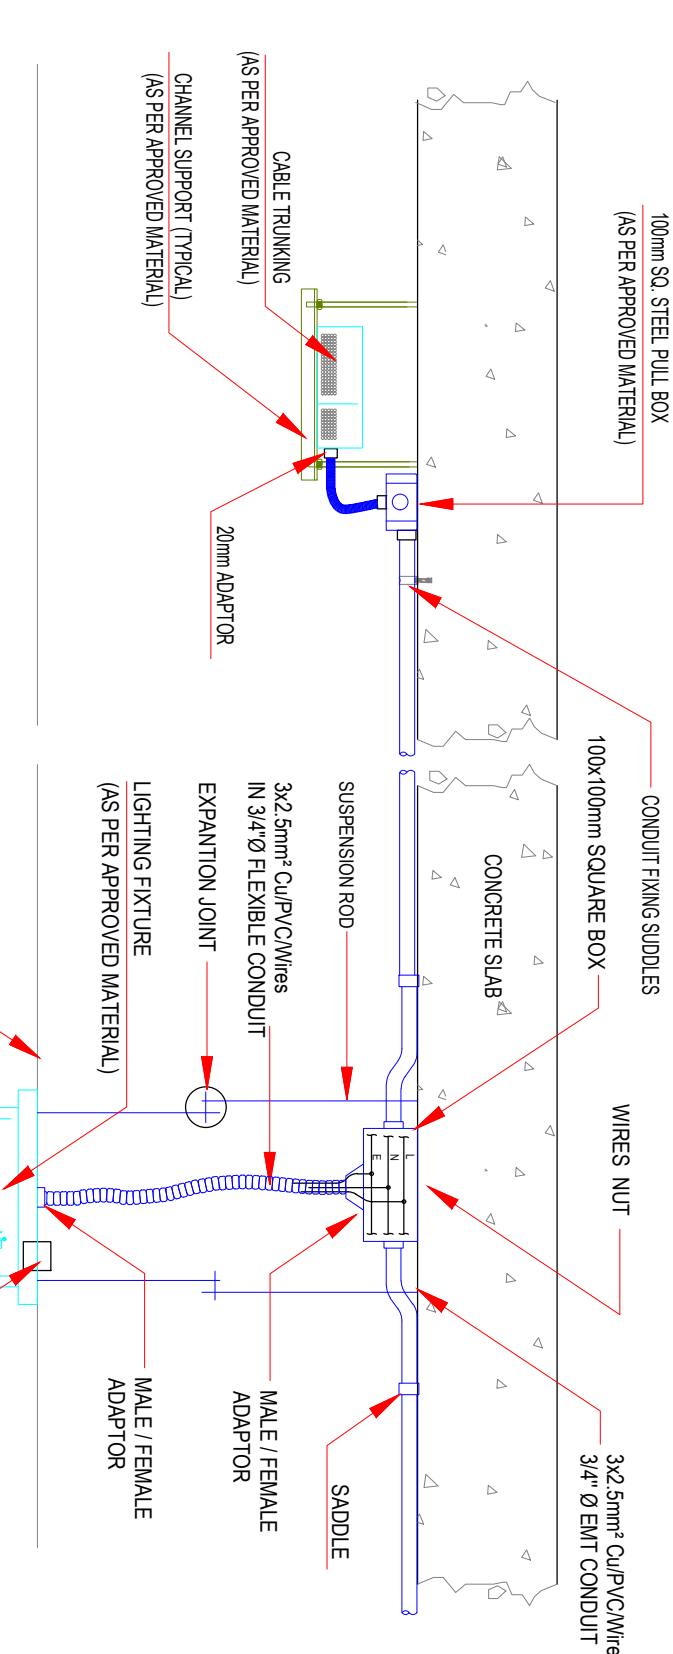


DIRECT-WALL / CEILING MOUNTING

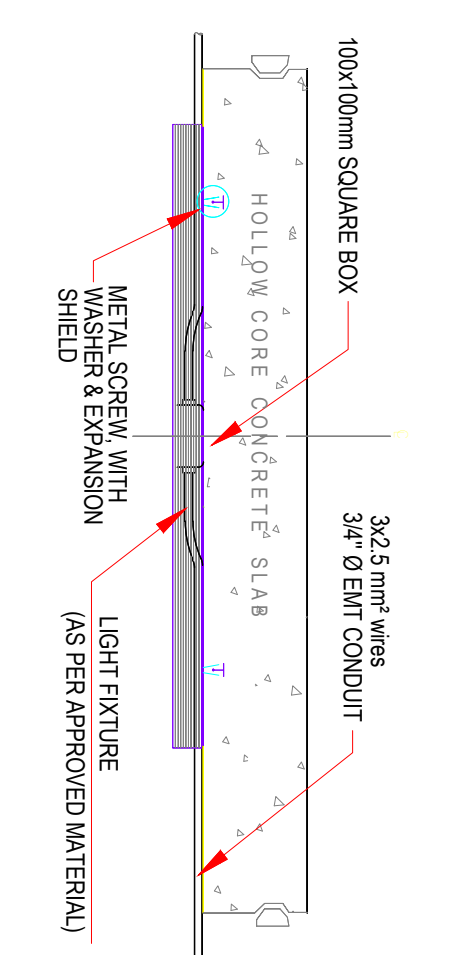

4 SUSPENDED EMERGENCY EXIT DETAIL

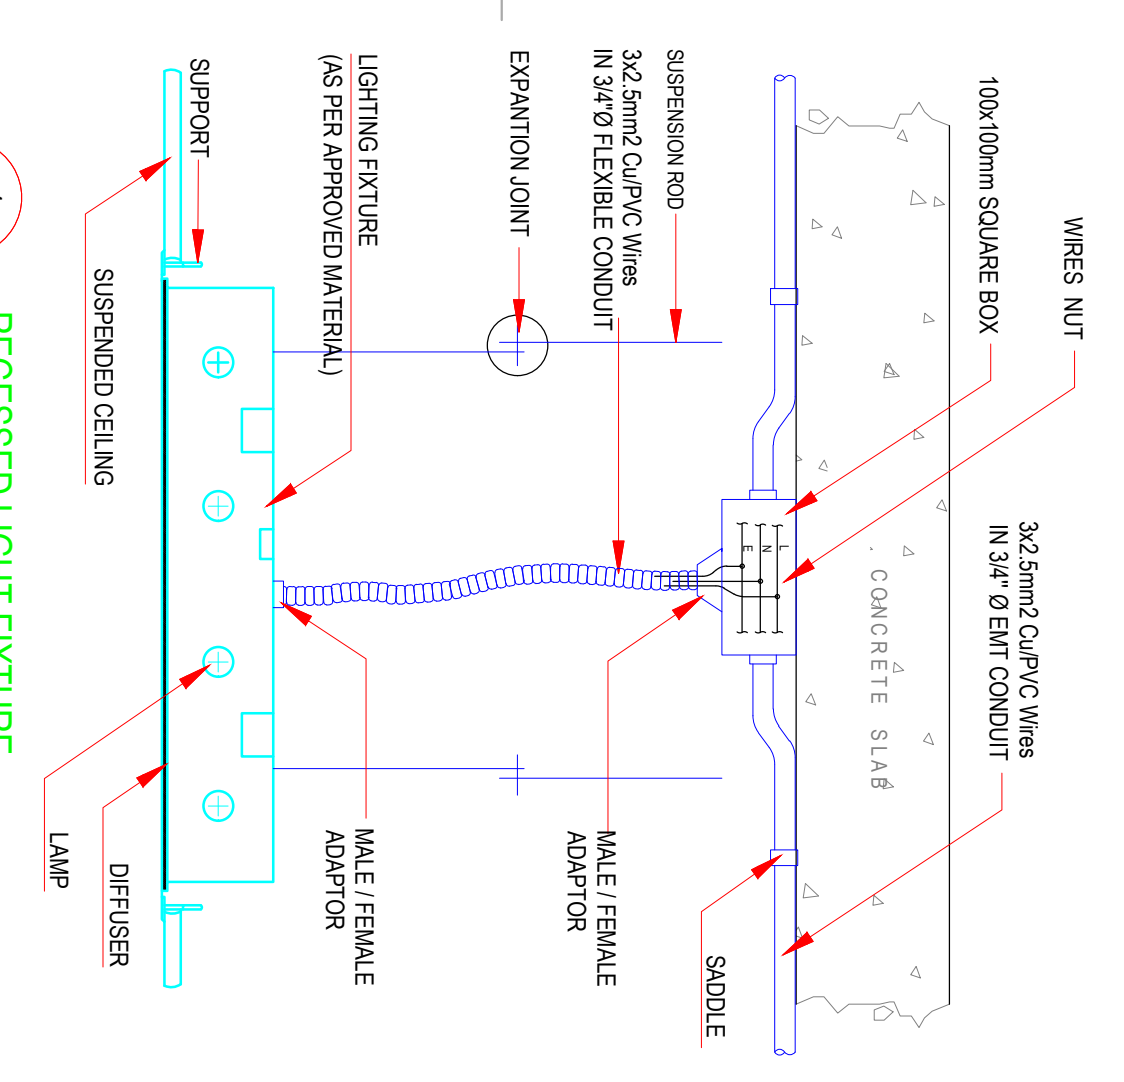


RECESSED LIGHT FIXTURE

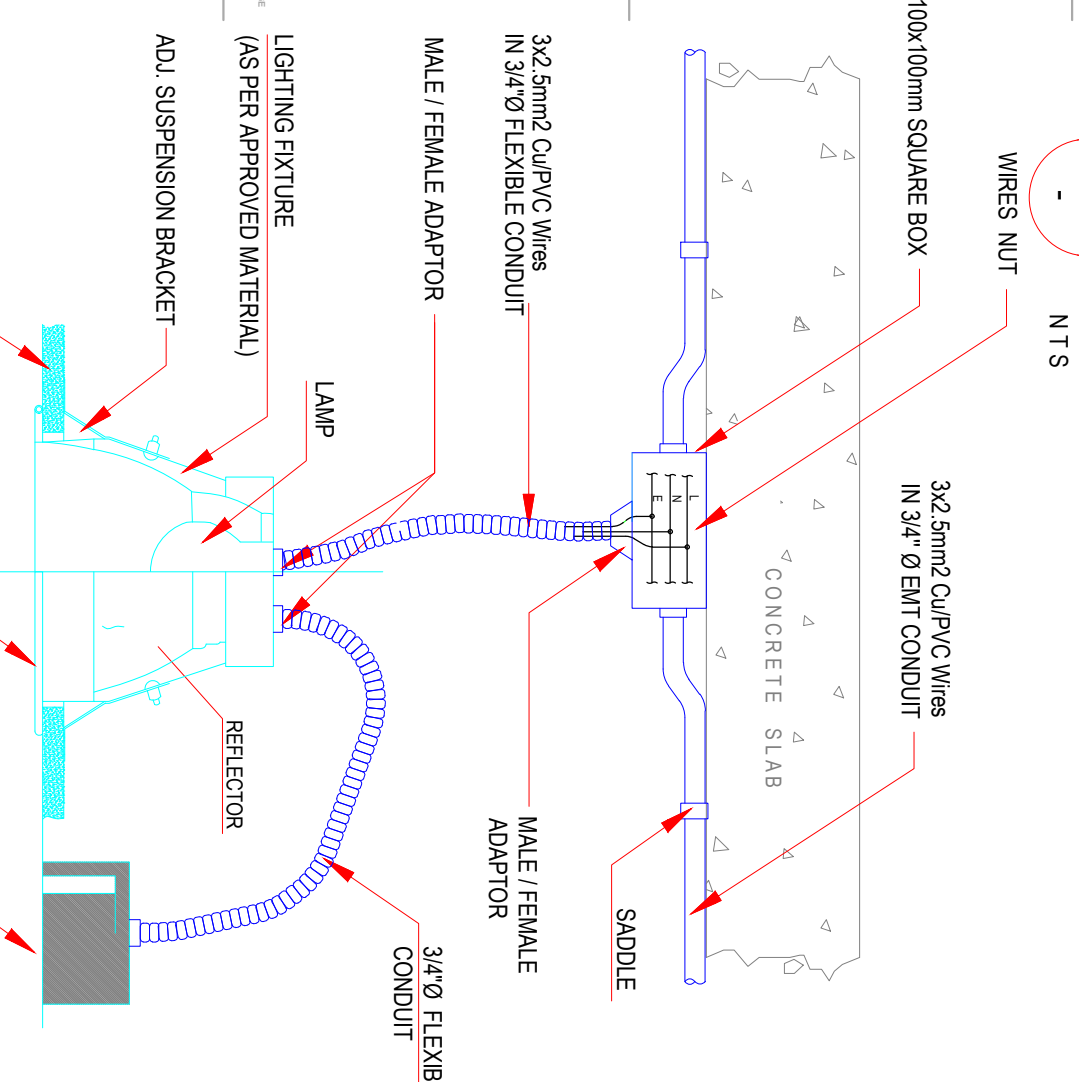

2
-
NTS

CEILING MOUNTED DOWNLIGHT

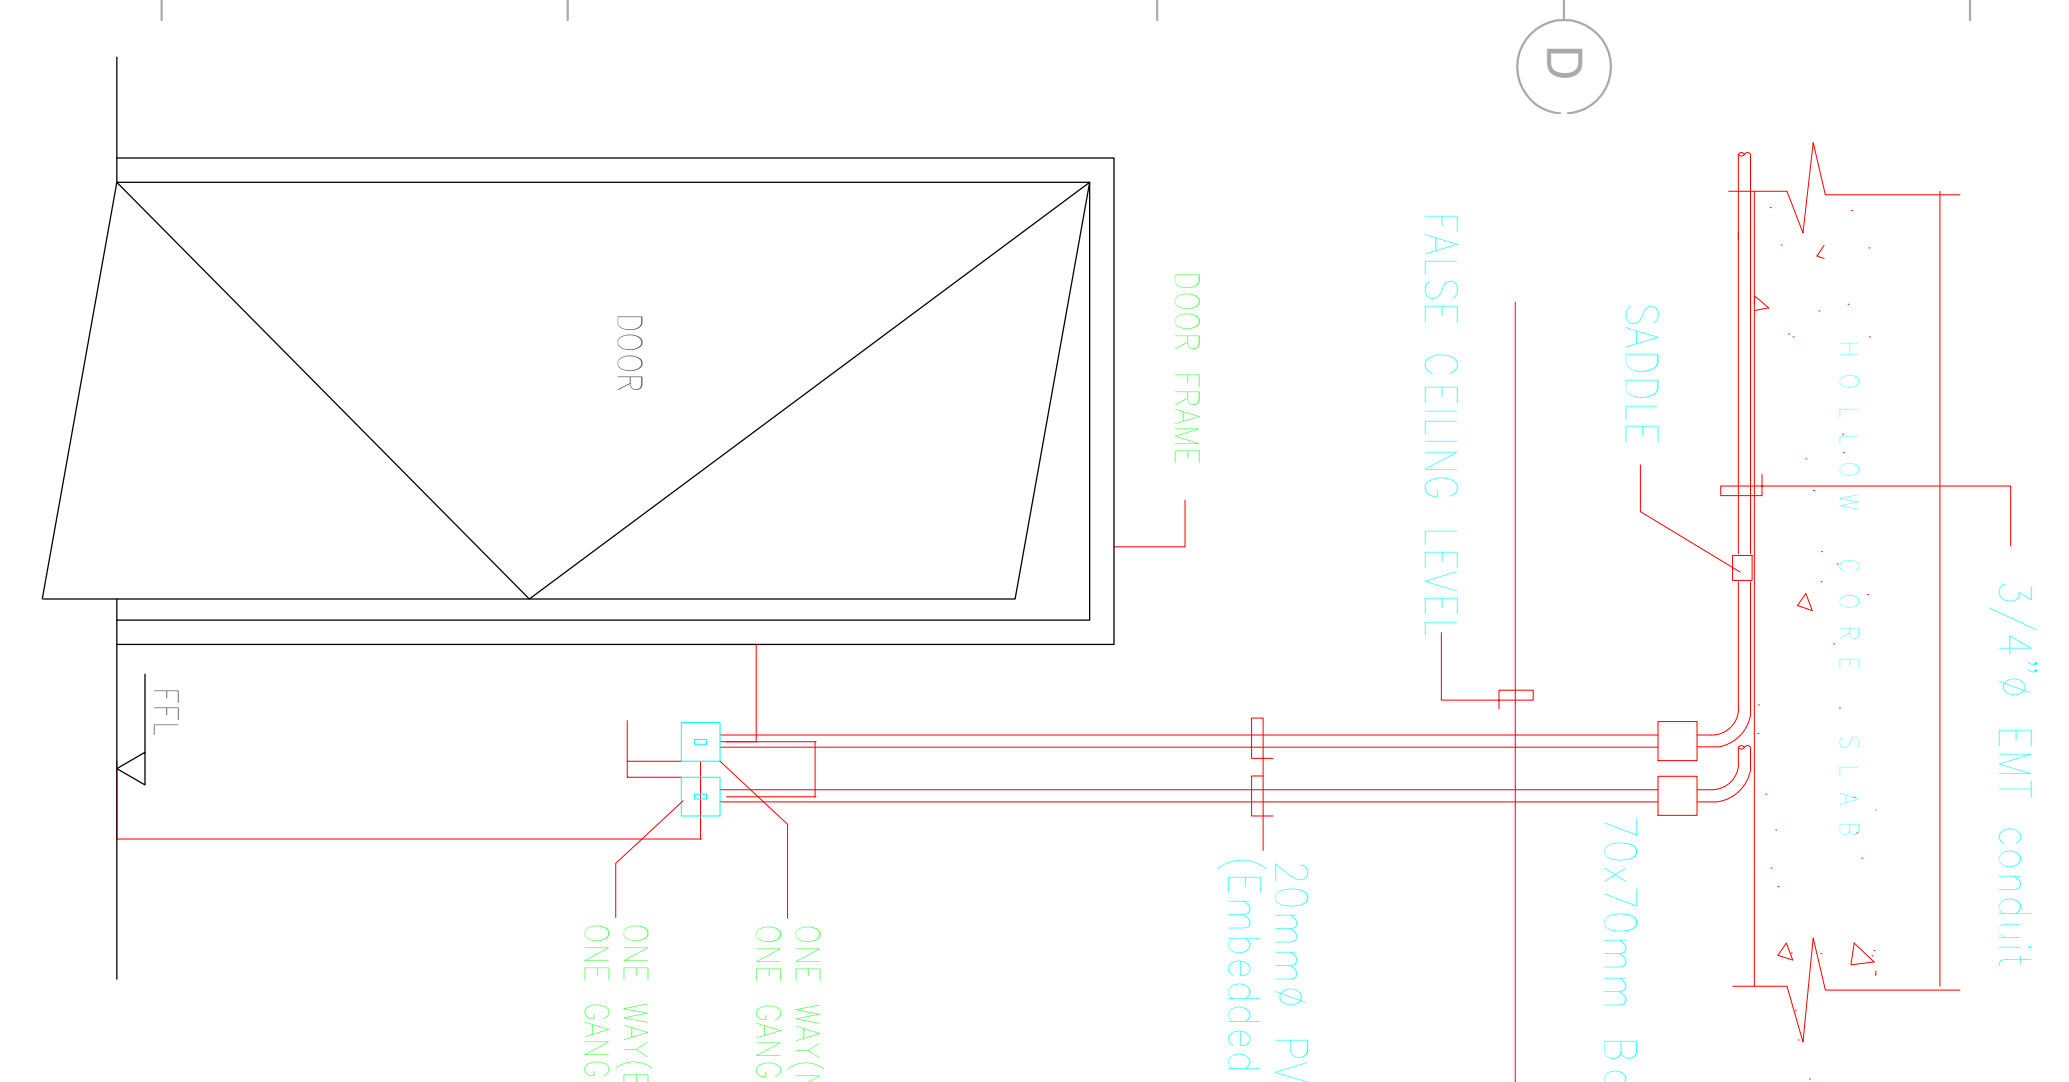

E LIGHT SWITCH MOUNTING TYPICAL DETAIL