

ASSIGNED FIXTURES (293)

- SUMMARY:**
- | | |
|-------------------------|-----|
| Total symbols: | 673 |
| Assigned: | 293 |
| Discarded: | 380 |
| Loops: | 10 |
| Rooms: | 181 |
| Specs: | 33 |
| Low confidence (<0.75): | 85 |
| Unlabeled: | 0 |


BY SPEC CODE

BY SPEC CODE:
W3: 212
S1: 64
S2: 16
C5: 1


BY ROOM TYPE:

BY ROOM TYPE:


E/S:	212
WC:	16
1R:	10
3Y:	8
8R:	6
13R:	6
9Y:	5
4Y:	5
5B:	4
22Y:	3
12B:	3
20R:	2
11B:	2
10Y:	2
6B:	2
7R:	2
23B:	1
18B:	1
29B:	1
DN:	1
14R:	1

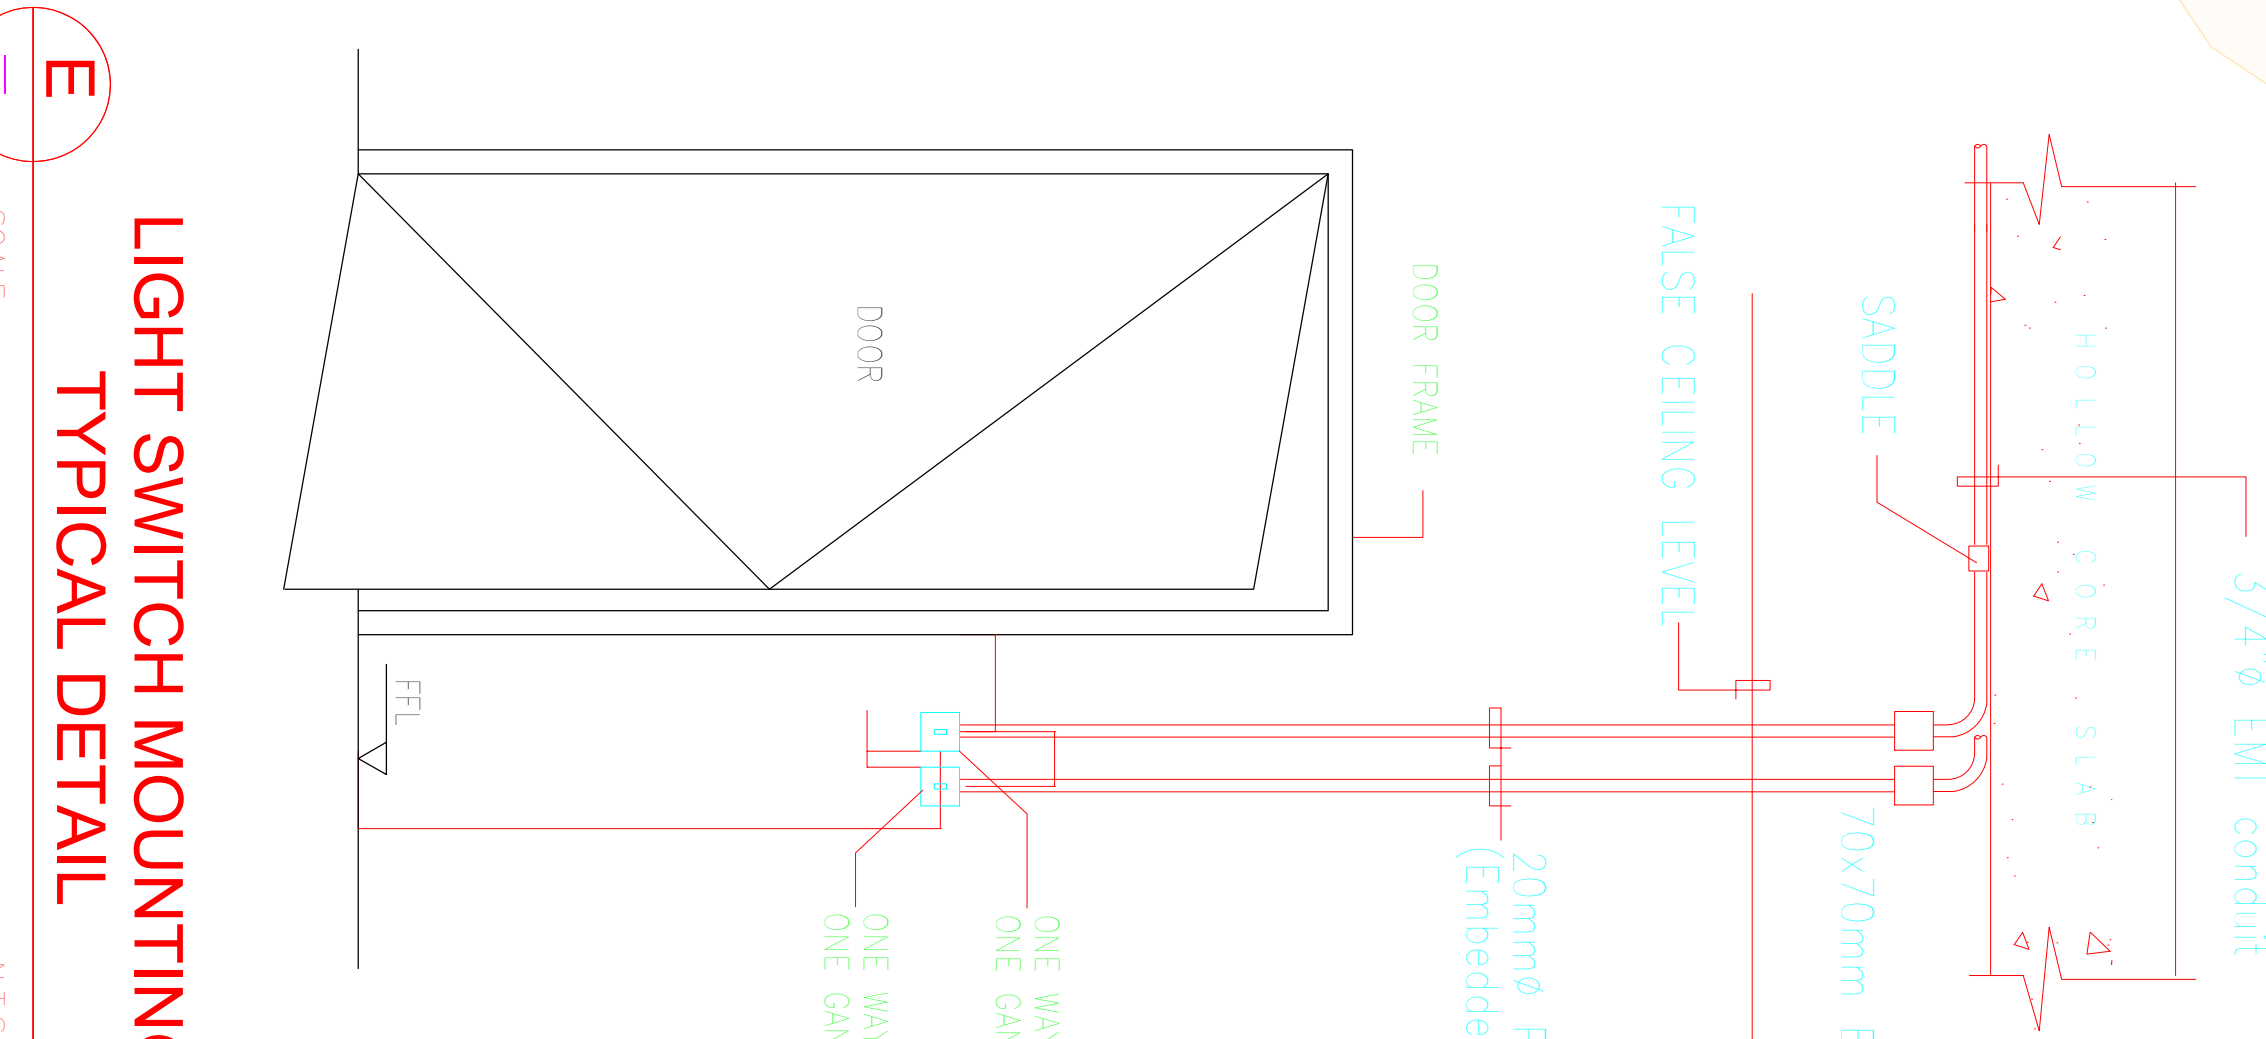

TYPICAL LIGHTING HOMERUN SECTION DETAILS

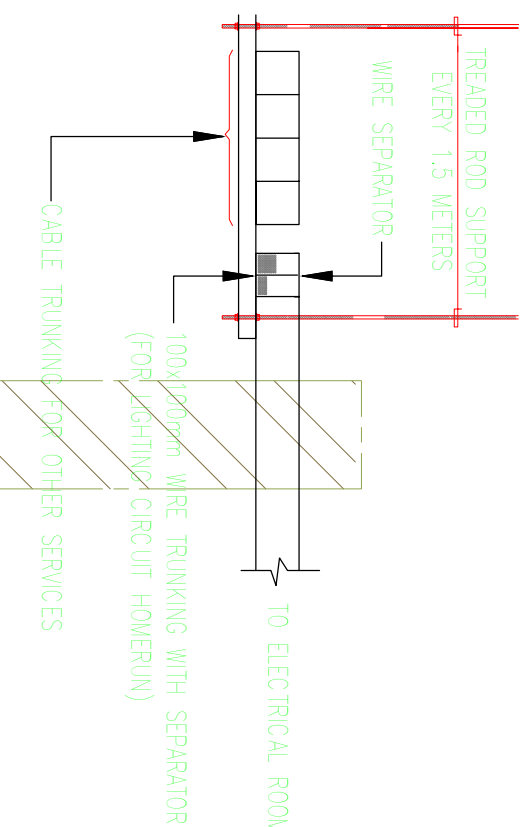

3 DIRECT-WALL / CEILING MOUNTING

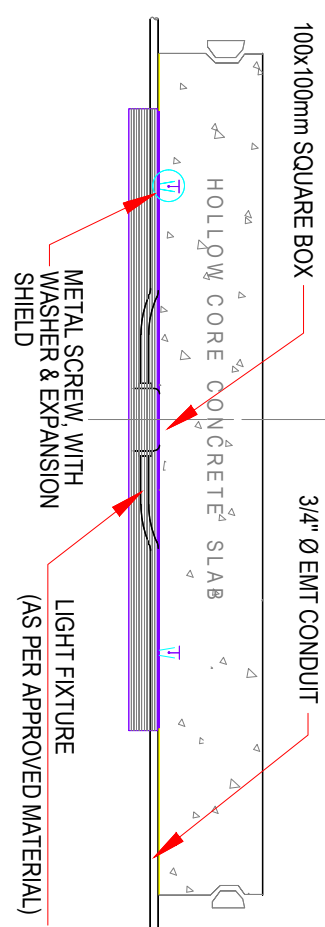

SUSPENDED EMERGENCY EXIT DETAIL

